
ELEKTRICKÁ SCHÉMA ROZVÁDZAČA A ROZPIS ISTIČOV • STN EN 61439-3 / STN EN 60617

TEST 3: RH – Hlavný domový rozvádzač (Rodinný dom 3F, 9 okruhov)

Pred elektromerom (QF0): 3P B25 A (Pred elektromerom) | V rozvádzači (QS1): Hlavný vypínač (3P 63 A) | Sústava: 3F (400 V, TN-C-S) | Prívod: CYKY-J 5x10 mm²

Číslo projektu: ESG-2026-041
Dátum: 04.11.2026
Kapacita skrine: 28 / 36 M (IP40)

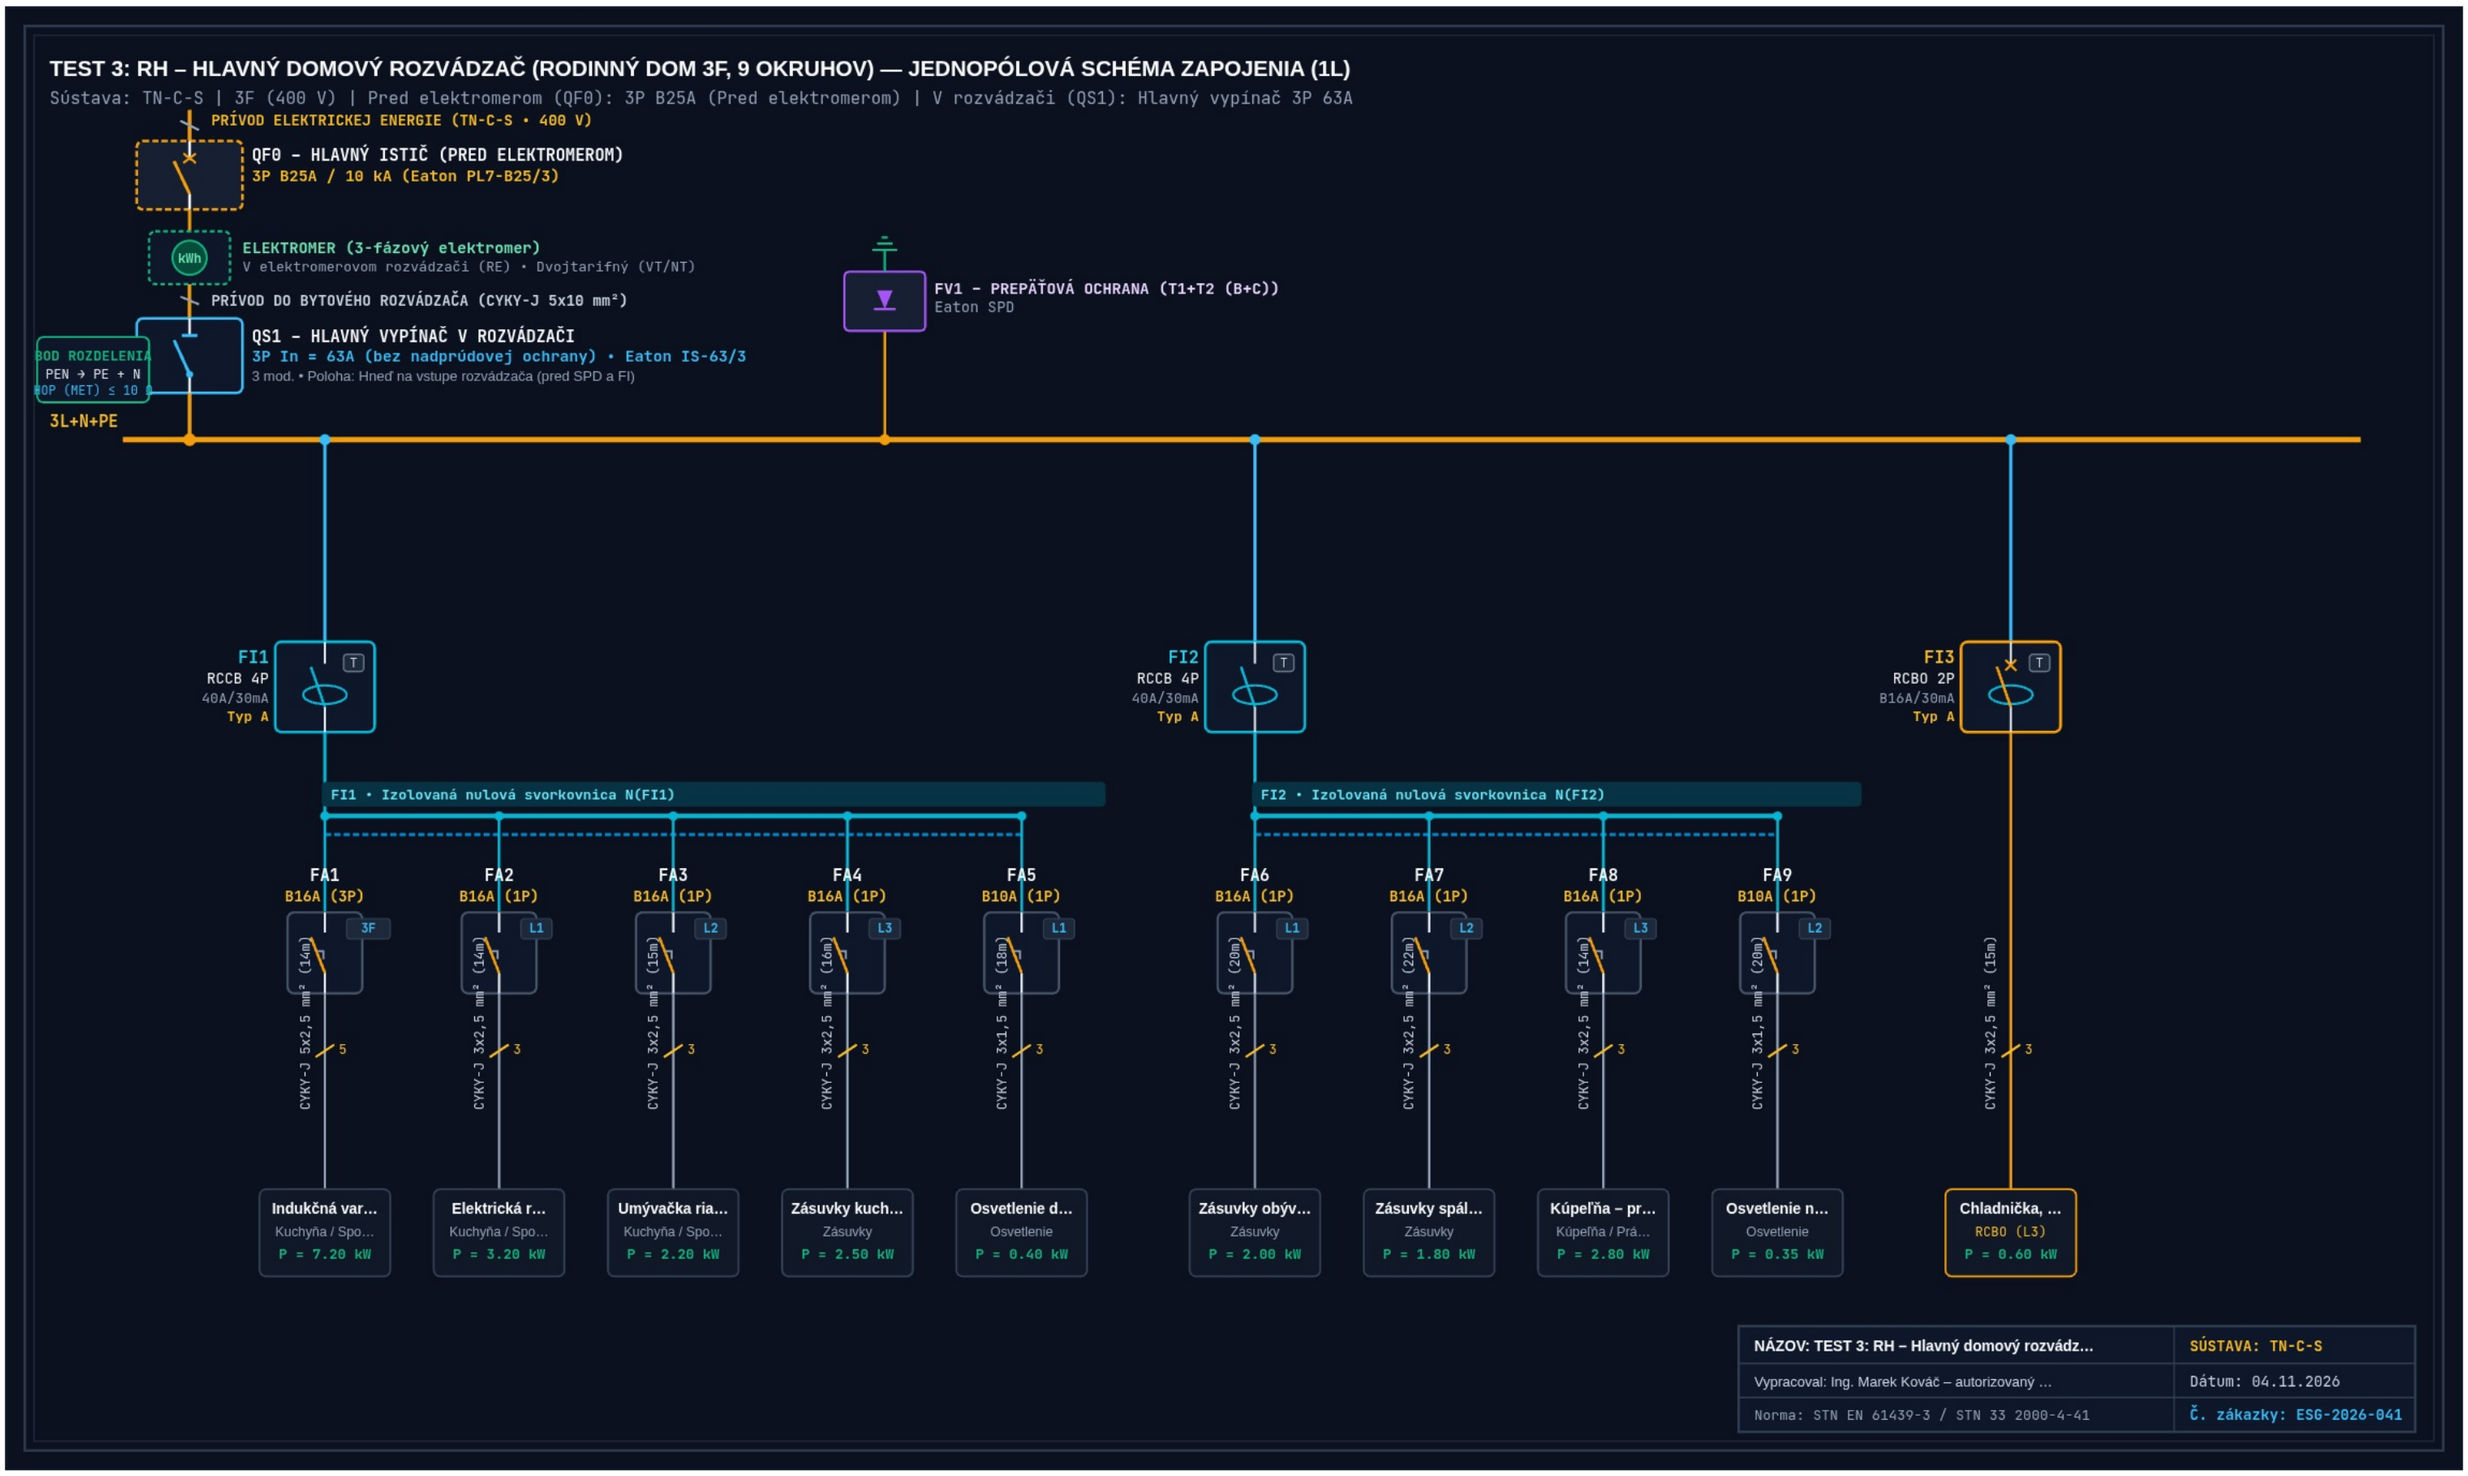

POPIS K SCHÉME — ROZPIS ISTIČOV A ELEKTRICKÝCH OKRUHOV (KTORÝ OKRUH JE NA KTOROM ISTIČI)

Istič	Ktorý okruh / spotrebič je na ističi	Typ a hodnota ističa	Prúdový chránič (RCD)	Fáza	Kábel a dĺžka	Príkon P	Prúd Ib / Iz	ΔU / Slučka Zs
FA1	Indukčná varná doska	3P B16 A (PL7-B16/3)	FI1 (40A / 30mA, Typ A)	L1,L2,L3	CYKY-J 5x2,5 mm² (14 m)	7.20 kW	11.3 A / 21.1 A	0.45% / 0.5 Ω
FA2	Elektrická rúra na pečenie	1P B16 A (PL7-B16/1)	FI1 (40A / 30mA, Typ A)	L1	CYKY-J 3x2,5 mm² (14 m)	3.20 kW	15.12 A / 24 A	1.21% / 0.5 Ω
FA3	Umývačka riadu	1P B16 A (PL7-B16/1)	FI1 (40A / 30mA, Typ A)	L2	CYKY-J 3x2,5 mm² (15 m)	2.20 kW	10.4 A / 24 A	0.89% / 0.518 Ω
FA4	Zásuvky kuchynská linka	1P B16 A (PL7-B16/1)	FI1 (40A / 30mA, Typ A)	L3	CYKY-J 3x2,5 mm² (16 m)	2.50 kW	11.81 A / 24 A	1.08% / 0.536 Ω
FA5	Osvetlenie denná časť (obývačka, kuchyňa, chodba)	1P B10 A (PL7-B10/1)	FI1 (40A / 30mA, Typ A)	L1	CYKY-J 3x1,5 mm² (18 m)	0.40 kW	1.83 A / 17.5 A	0.32% / 0.786 Ω
FA6	Zásuvky obývacia izba a pracovňa	1P B16 A (PL7-B16/1)	FI2 (40A / 30mA, Typ A)	L1	CYKY-J 3x2,5 mm² (20 m)	2.00 kW	9.45 A / 24 A	1.08% / 0.607 Ω
FA7	Zásuvky spálňa a detské izby	1P B16 A (PL7-B16/1)	FI2 (40A / 30mA, Typ A)	L2	CYKY-J 3x2,5 mm² (22 m)	1.80 kW	8.51 A / 24 A	1.07% / 0.643 Ω
FA8	Kúpeľňa – práčka, sušička a zásuvky	1P B16 A (PL7-B16/1)	FI2 (40A / 30mA, Typ A)	L3	CYKY-J 3x2,5 mm² (14 m)	2.80 kW	13.23 A / 24 A	1.06% / 0.5 Ω
FA9	Osvetlenie nočná časť (spálňa, izby, kúpeľňa)	1P B10 A (PL7-B10/1)	FI2 (40A / 30mA, Typ A)	L2	CYKY-J 3x1,5 mm² (20 m)	0.35 kW	1.6 A / 17.5 A	0.32% / 0.845 Ω
FI3	Chladnička, mraznička & alarm (samostatný RCBO)	RCBO 2P B16 A (PFL7-16/1N/B/003-A)	Integrovaný RCBO 30mA (Typ A)	L3	CYKY-J 3x2,5 mm² (14 m)	0.60 kW	2.61 A / 24 A	0.35% / 0.52 Ω

ZODPOVEDNÝ PROJEKTANT:	NÁZOV VÝKRESU / ROZVÁDZAČA:	ČÍSLO VÝKRESU / FORMÁT:	ODBORNÉ OVERENIE (STN 33 2000-6):
Ing. Marek Kováč – autorizovaný elektroprojektant Miesto stavby: Bratislava	TEST 3: RH – Hlavný domový rozvádzač (Rodinný dom 3F, 9 okruhov) Sústava: 3F / 400 V / TN-C-S	ESG-2026-041 • A3 Dátum: 04.11.2026	Pečiatka a podpis revízneho technika